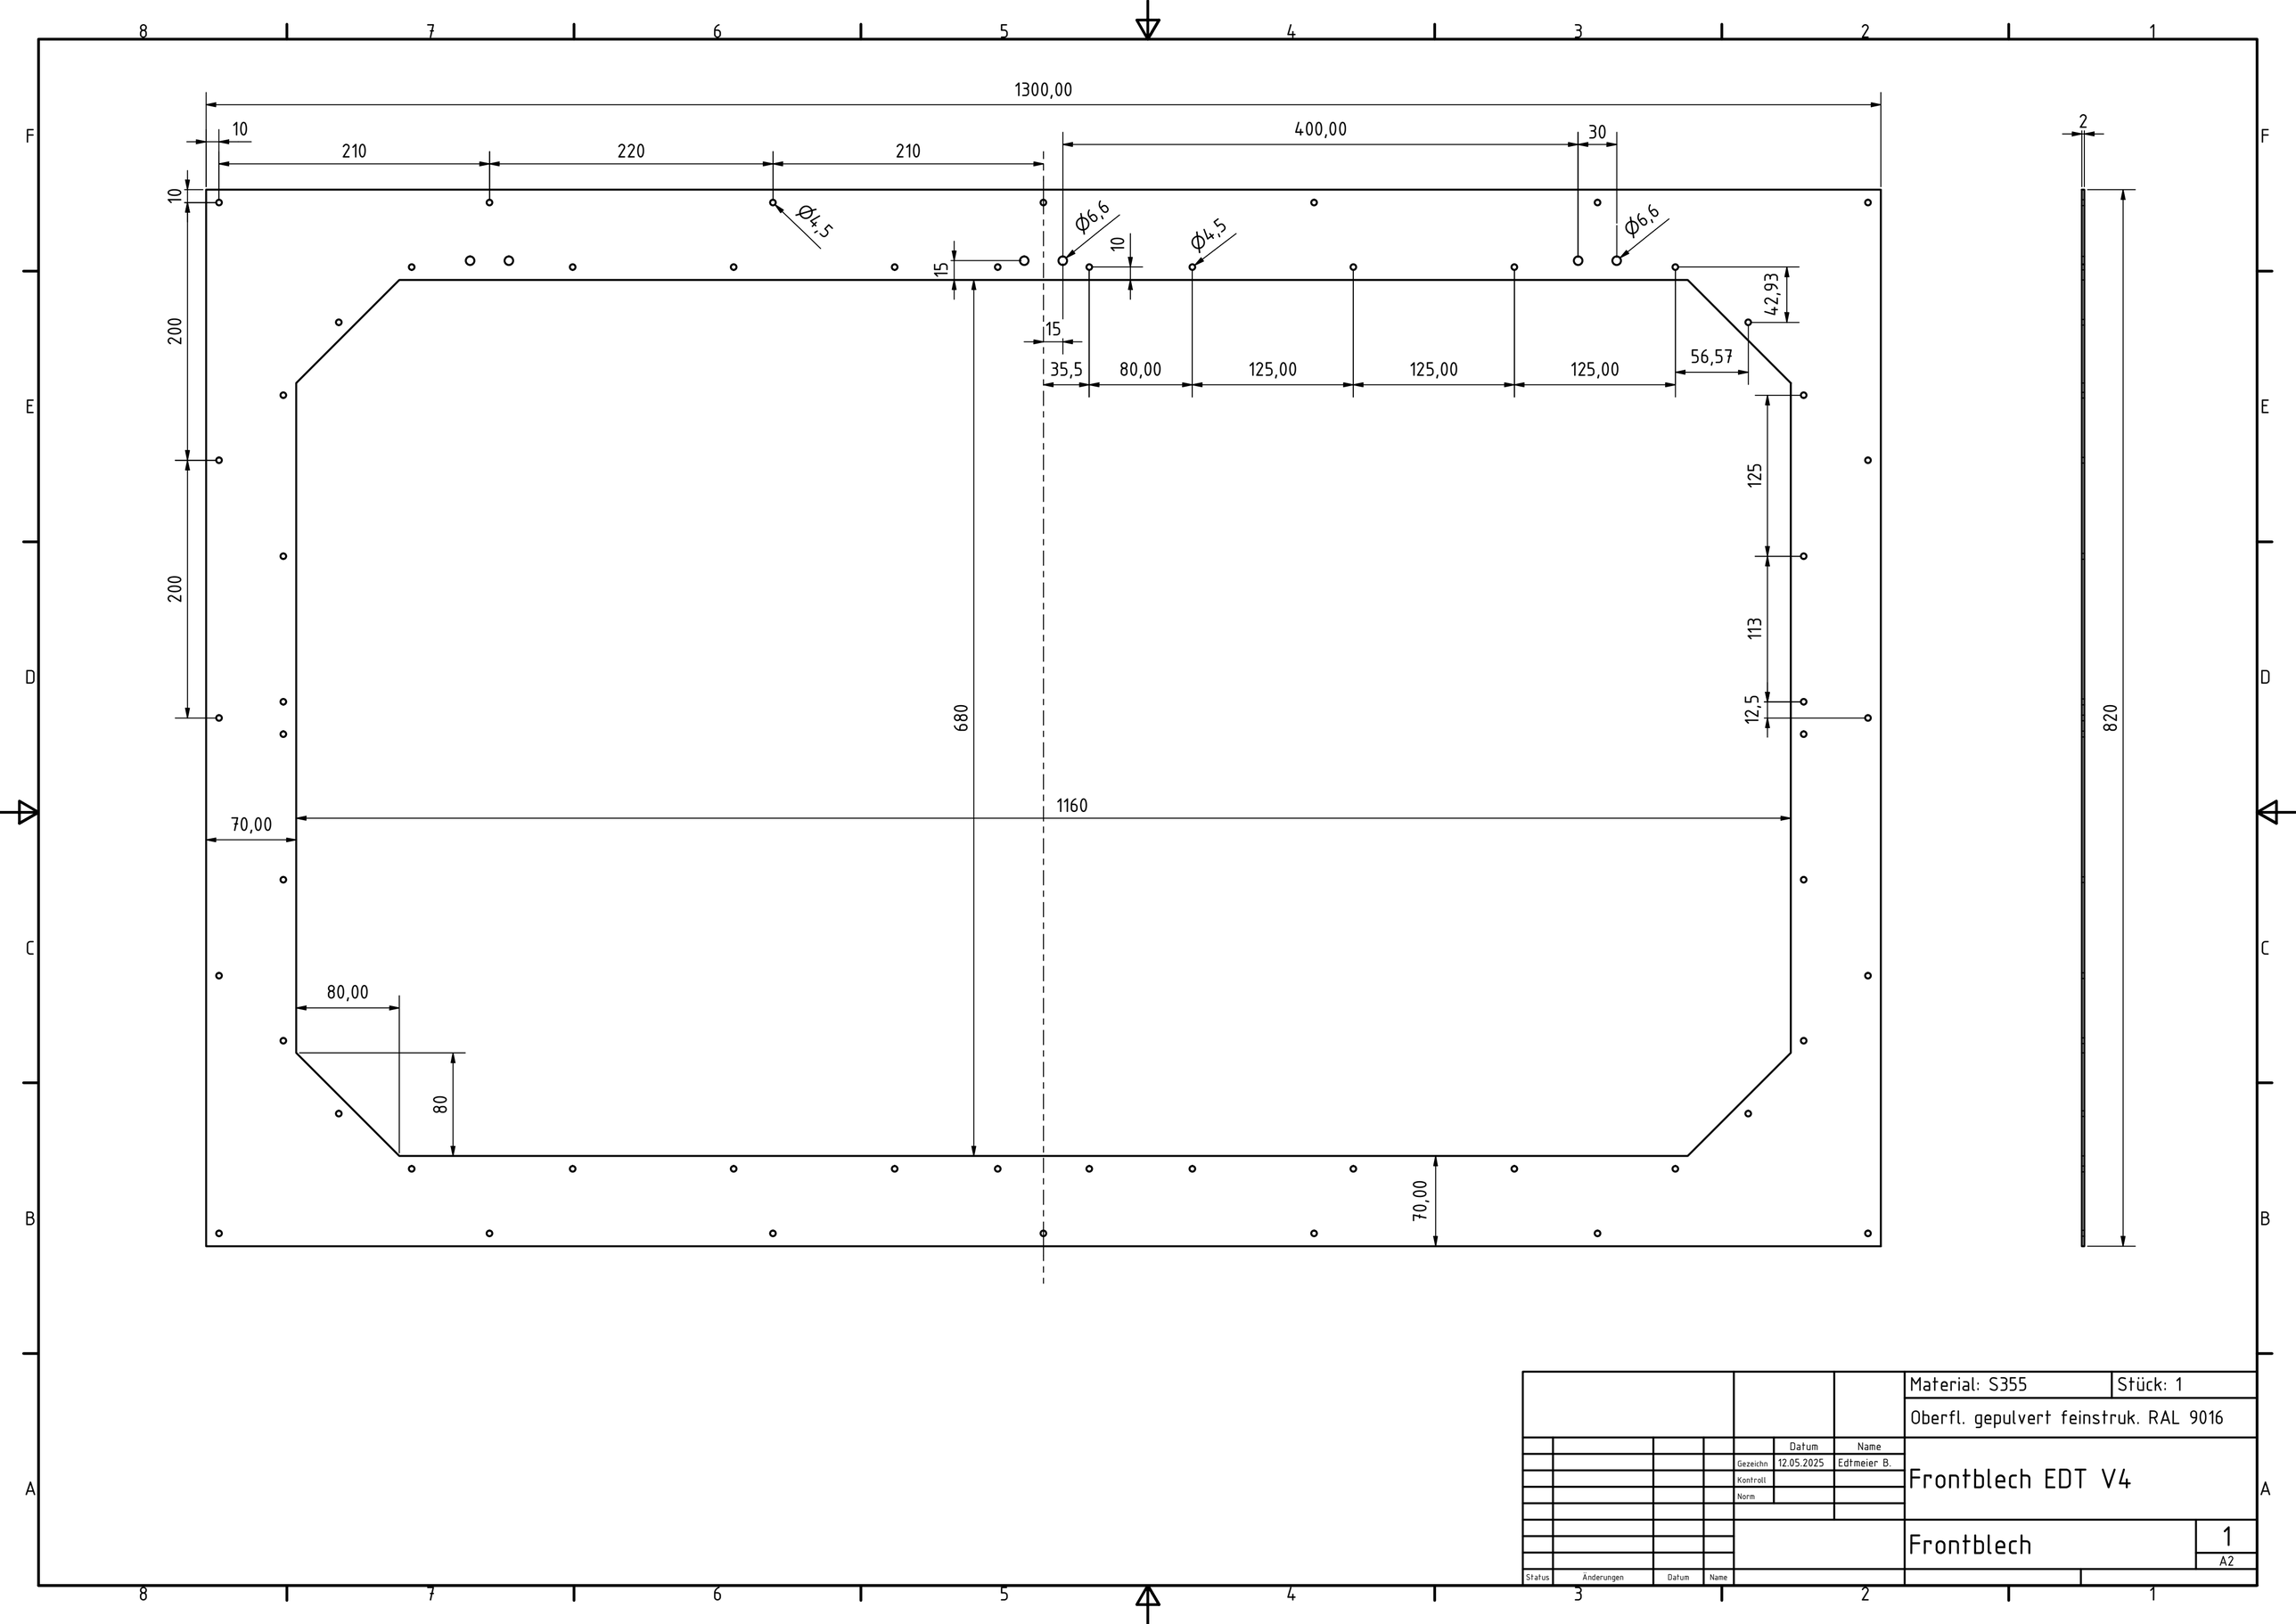

						Material: S355	Stück: 1
						Oberfl. gepulvert feinstruk. RAL 9016	
					Datum	Name	
				Gezeichn	12.05.2025	Edtmeier B.	Frontblech EDT V4
				Kontroll			
				Norm			
						Frontblech	1
							A2
Status	Änderungen	Datum	Name				